



## ITEM 8.06 - HANGING GANTRY OVER 'HONEST EATS' COUNTER


- 20mm MILD STEEL BAR
- METAL MESH 2-TIER SHELVING
- UNIT POWDER COATED THROUGHOUT (RAL 9011)
- BASE OF SHELF @ 2200 A.F.F.L.

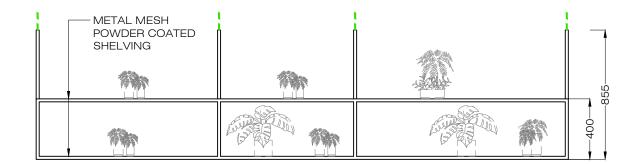


**ELEVATION A** 

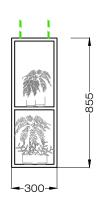

**ELEVATION B** 

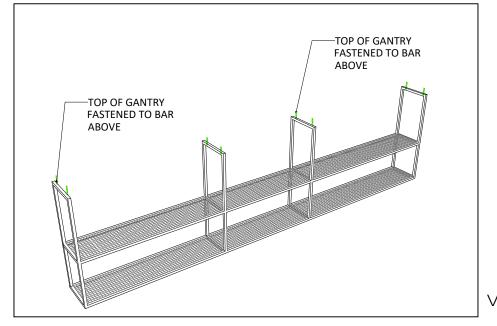

VISUAL

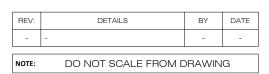

CLIENT:

TITLE:

JOHN PAUL CONSTRUCTION

'HONEST EATS' GANTRY FABRICATION

DRAWING NUMBER: 5290-02-FAB11 SCALE: 1:25@A3

DATE: 08-02-2023 DWG BY: NC STATUS: CONST

